
TEDARİK KAPSAMI: 2 sıra temel kalıbı üzerinde Nudura 8in Standard dış duvarlar ve 6in Standard ortak / merdiven / asansör duvarları; TAM kalıp olarak teslim edilir ve sahada bu çizimlere göre kesilir; aksesuarlar; BuildEase modelleme ve ön kesim desteği. Beton, donatı, betonarme döşemeler, balkonlar, merdivenler, blok bölme duvarlar, pencere ve kapılar başkalarınca yapılır (koordinasyon için gösterilmiştir). Statik tasarım (Türkiye Bina Deprem Yönetmeliği), TS 825 ve yangın yönetmeliğine göre müşterinin mühendislerince yapılır.

TEKLİF - UYGULAMA İÇİN DEĞİLDİR

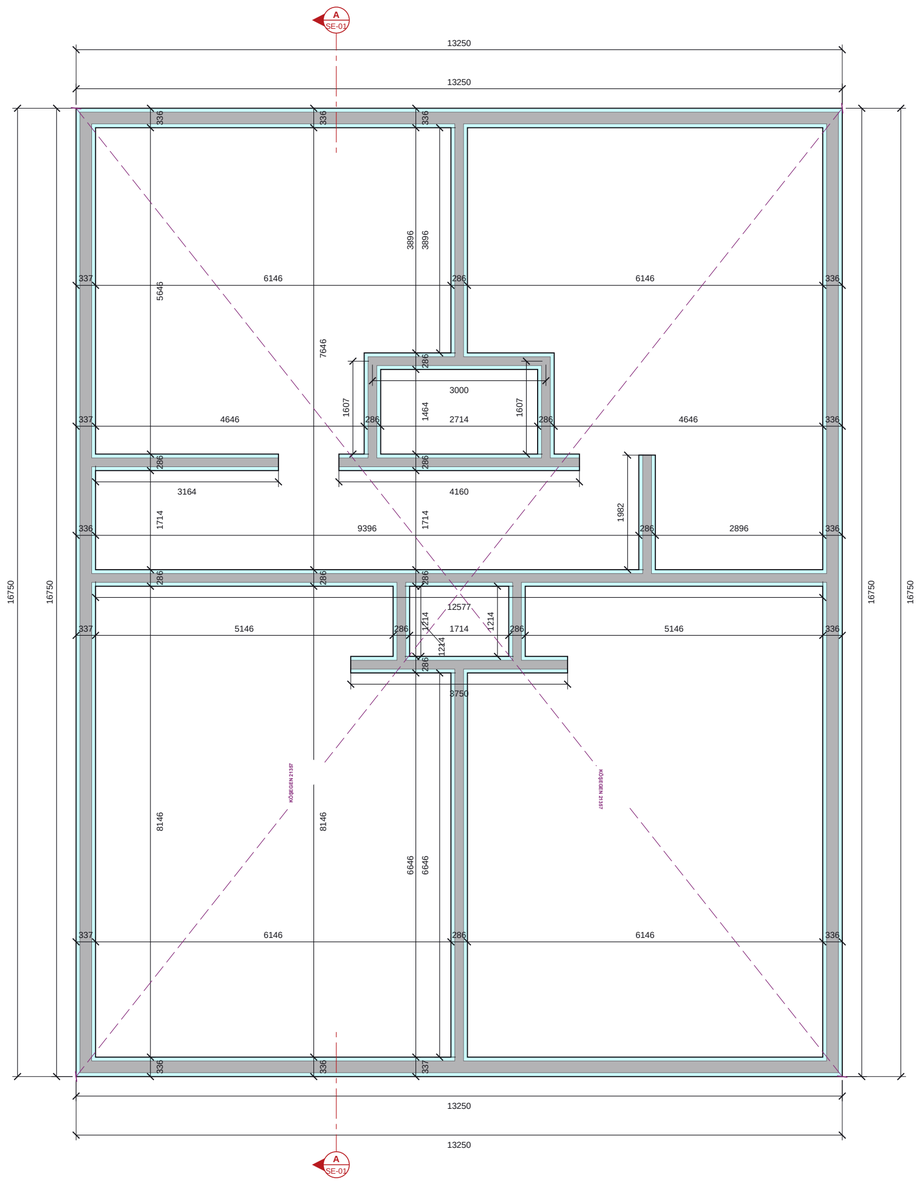

EPS yalıtım (Nudura kalıp)
Beton çekirdek
Boşlukta uç kapağı
Taşıyıcı yığma duvar (bağlam)
Mühendis ayak donatısı (ICF ayakta n-H12 düşey) / WS filiz
Aplikasyon kontrol köşegeni (dış ICF köşeleri)
Kesit hattı (SE paftasına bakın)

TEMEL KALIPLARI (2 SIRA) ICF PLANI

Ölçek 1:75 @ A2 | Plan kesiti -3307

0 1 2 3 4m

Ölçekle düşmeyin. Tüm ölçüler milimetre, kotlar zemin kat FFL'den metre cinsindendir. Tüm ölçüleri kahsida kontrol edin.

TEMEL KALIPLARI (2 SIRA) ICF LİSTELERİ

BOŞLUK LİSTESİ

Ref	Genişlik	Yükseklik	Derinlik	Üst kot	Lento
yok					

ICF'deki yapısal boşluklar; denizlik ve üst kot zemin kat FFL'ye göre.

NOTLAR

1. ICF: Nudura 8" Std, 66.7 EPS + 203.2 çekirdek + 66.7 EPS = 336.6; 6" Std, 66.7 EPS + 152.4 çekirdek + 66.7 EPS = 285.8. Ölçüler ICF yüzlerinedir.
2. Kotlar zemin kat FFL'ye göre. Denizlik / üst kot = ICF'deki yapısal boşluk.
3. Statik proje yayınlanmadı (henüz yapı ruhsatı yok). ICF, Arfa Yapi mimari setine göre (paftalar 02-14/14): çizilen her 250 taşıyıcı duvar ICF - 8in Std (203 çekirdek = istenen 20 cm çekirdek) dış duvarlar, 6in Std ortak / merdiven / asansör duvarları; 20 cm yerinde dökme betonarme döşemeler çekirdeklere oturur. Donatı ve deprem tasarımı müşterinin mühendisince yapılır.
4. Lento (L-n) ve çelik (B-n, C-1) işaretleri rev -'den alınmıştır; o esas alınır.
5. Yığma duvarlar bağlam için gösterilmiştir.
6. Referans: +-0.00 = saha kotu (çizimler); bahçe katı FFL -1.75, zemin kat FFL +1.00, kat yüksekliği 2.75 m.
7. ICF, dış duvarların çizilen dış yüzünde (8in Std 337 / çizimde 250) - odalar cephede 87 mm kaybeder.

REVİZYONLAR

REV	TARİH	AÇIKLAMA
Q01	22.10.26	İlk yayın - bir blok Rev C / 12 blok Rev B

Nudura™ BuildEase

MÜŞTERİ	PROJE
Arfa Yapi Sistemleri - Tremco CPG Türkiye aracılığıyla	Arfa Yapi konut blokları, Bayraklı, İzmir - Blok

PAFTA BAŞLIĞI
TEMEL KALIPLARI (2 SIRA) ICF GENEL YERLEŞİM PLANI

ÖLÇEK	BOYUT	TARİH
1:75	A2	22.10.26
ÇİZEN	KONTROL	ONAY
TS		

DURUM	PAFTA NO.	REV
TEKLİF	ES26-085-GA-01	Q01