

TEDARİK KAPSAMI: 2 sıra temel kalıbı üzerinde Nudura 8in Standard dış duvarlar ve 6in Standard ortak / merdiven / asansör duvarları; TAM kalıp olarak teslim edilir ve sahada bu çizimlere göre kesilir; aksesuarlar; BuildEase modelleme ve ön kesim desteği. Beton, donatı, betonarme döşemeler, balkonlar, merdivenler, blok bölme duvarlar, pencere ve kapılar başkalarınca yapılır (koordinasyon için gösterilmiştir). Statik tasarım (Türkiye Bina Deprem Yönetmeliği), TS 825 ve yangın yönetmeliğine göre müşterinin mühendislerince yapılır.

TEKLİF - UYGULAMA İÇİN DEĞİLDİR

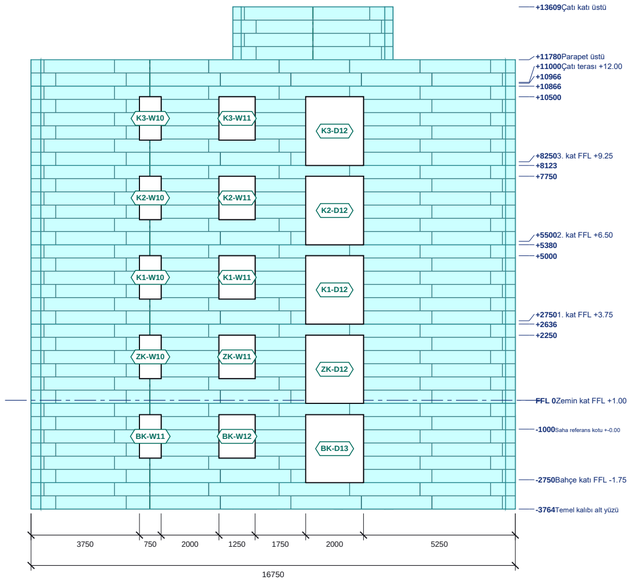

GÖRÜNÜŞ - 11 AKSI CEPHESİ

Ölçek 1:150 @ A2 | Kotlar zemin kat FFL'ye göre; denizlik ve üst kotlar listede

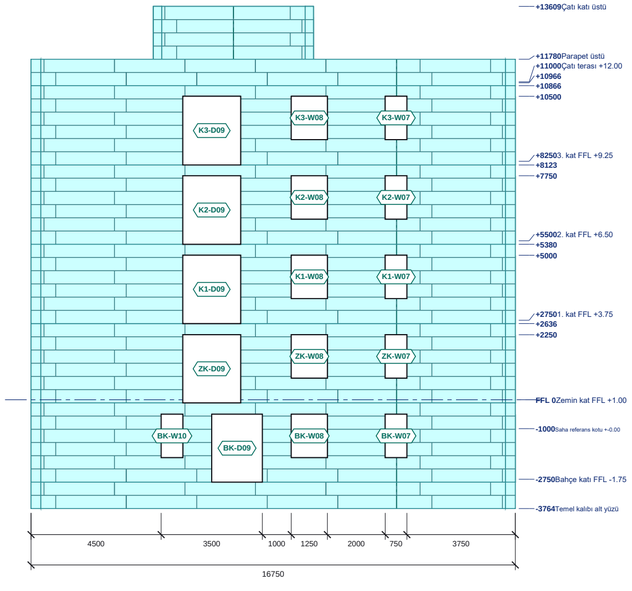

GÖRÜNÜŞ - 1 AKSI CEPHESİ (GİRİŞ)

Ölçek 1:150 @ A2 | Kotlar zemin kat FFL'ye göre; denizlik ve üst kotlar listede

0 1 2 3 4 5 6 7 8m

ICF dış EPS yüzü
Blok sıra derzi
Düşey derz

Ölçekle ölçmeyin. Tüm ölçüler milimetre. Kotlar zemin kat FFL'den metre cinsindendir. Tüm ölçüleri sahada kontrol edin.

GÖRÜNÜŞ LİSTELERİ

GÖRÜNÜŞ - 11 AKSI CEPHESİ: BOŞLUKLAR

Ref	Genişlik	Yükseklik	Denizlik	Üst kot	Lento
BK-D13	2000	2350	-2850	+-500	-
BK-W11	750	1500	-2000	+-500	-
BK-W12	1250	1500	-2000	+-500	-
K1-W10	750	1500	+3500	+5000	-
K1-W11	1250	1500	+3500	+5000	-
K1-D12	2000	2364	+2636	+5000	-
K2-W10	750	1500	+6250	+7750	-
K2-W11	1250	1500	+6250	+7750	-
K2-D12	2000	2370	+5380	+7750	-
K3-W10	750	1500	+9000	+10500	-
K3-W11	1250	1500	+9000	+10500	-
K3-D12	2000	2377	+8123	+10500	-
ZK-D12	2000	2357	-107	+2250	-
ZK-W10	750	1500	+750	+2250	-
ZK-W11	1250	1500	+750	+2250	-

ICF'deki yapısal boşluklar; denizlik ve üst kot zemin kat FFL'ye göre.

GÖRÜNÜŞ - 1 AKSI CEPHESİ (GİRİŞ): BOŞLUKLAR

Ref	Genişlik	Yükseklik	Denizlik	Üst kot	Lento
BK-D09	1750	2350	-2850	+-500	-
BK-W07	750	1500	-2000	+-500	-
BK-W08	1250	1500	-2000	+-500	-
BK-W10	750	1500	-2000	+-500	-
K1-W07	750	1500	+3500	+5000	-
K1-W08	1250	1500	+3500	+5000	-
K1-D09	2000	2364	+2636	+5000	-
K2-W07	750	1500	+6250	+7750	-
K2-W08	1250	1500	+6250	+7750	-
K2-D09	2000	2370	+5380	+7750	-
K3-W07	750	1500	+9000	+10500	-
K3-W08	1250	1500	+9000	+10500	-
K3-D09	2000	2377	+8123	+10500	-
ZK-D09	2000	2357	-107	+2250	-
ZK-W07	750	1500	+750	+2250	-
ZK-W08	1250	1500	+750	+2250	-

ICF'deki yapısal boşluklar; denizlik ve üst kot zemin kat FFL'ye göre.

GÖRÜNÜŞ - 11 AKSI CEPHESİ: KOTLAR

Kot	FFL
Temel kalıbı alt yüzü	-3764
Bahçe katı FFL -1.75	-2750
Saha referans kotu +-0.00	-1000
Zemin kat FFL +1.00	0
ICF üstü	+2250
ICF üstü	+2636
1. kat FFL +3.75	+2750
ICF üstü	+5000
ICF üstü	+5380
2. kat FFL +6.50	+5500
ICF üstü	+7750
ICF üstü	+8123
3. kat FFL +9.25	+8250
ICF üstü	+10500
ICF üstü	+10866
çatı katmanları üstü	+10966
Çatı terası +12.00	+11000
Parapet üstü	+11780
Çatı katı üstü	+13609

GÖRÜNÜŞ - 1 AKSI CEPHESİ (GİRİŞ): KOTLAR

Kot	FFL
Temel kalıbı alt yüzü	-3764
Bahçe katı FFL -1.75	-2750
Saha referans kotu +-0.00	-1000
Zemin kat FFL +1.00	0
ICF üstü	+2250
ICF üstü	+2636
1. kat FFL +3.75	+2750
ICF üstü	+5000
ICF üstü	+5380
2. kat FFL +6.50	+5500
ICF üstü	+7750
ICF üstü	+8123
3. kat FFL +9.25	+8250
ICF üstü	+10500
ICF üstü	+10866
çatı katmanları üstü	+10966
Çatı terası +12.00	+11000
Parapet üstü	+11780
Çatı katı üstü	+13609

NOTLAR

1. ICF: Nudura 8" Std, 66.7 EPS + 203.2 çekirdek + 66.7 EPS = 336.6; 6" Std, 66.7 EPS + 152.4 çekirdek + 66.7 EPS = 285.8. Dış EPS yüzü blok sıra derzleri, düşey
   blok derzleri ve istif derzleri ile yerleşime göre gösterilmiştir.
2. Kotlar zemin kat FFL'ye göre. Boşluklar ICF'deki yapısal boşluklardır; cam, kapı, sıva
   ve kaplamalar başkalarınca yapılır, gösterilmemiştir.
3. Yığma duvarlar modellendiği gibi gösterilmiştir.
4. Aplikasyon, lento ve çelik için ES26-085-GA-01'e bakın.
5. Referans: +-0.00 = saha kotu (çizimler); bahçe katı FFL -1.75, zemin kat FFL +1.00,
   kat yüksekliği 2.75 m.
6. ICF, dış duvarların çizilen dış yüzünde (8in Std 337 / çizimde 250) - odalar cephede 87 mm kaybeder.

REVİZYONLAR

REV	TARİH	AÇIKLAMA
Q01	22.10.26	İlk yayın - bir blok Rev C / 12 blok Rev B

Nudura™ BuildEase

MÜŞTERİ	PROJE
Arfa Yapi Sistemleri - Tremco CPG Türkiye aracılığıyla	Arfa Yapi konut blokları, Bayraklı, İzmir - Blok

PAFTA BAŞLIĞI

DOĞU VE BATI GÖRÜNÜŞLERİ

Boşluklar, kotlar ve çatı katmanları ile ICF görünüşleri

ÖLÇEK	BOYUT	TARİH
1:150	A2	22.10.26
ÇİZEN	KONTROL	ONAY
TS		

DURUM	PAFTA NO.	REV
TEKLİF	ES26-085-EL-02	Q01