
SUPPLY SCOPE: Nudura 8in Standard external walls and 6in Standard party / stair / lift walls on 2 courses of footing forms, delivered as FULL forms and cut on site to these drawings; accessories; BuildEase modelling and pre-cut support. Concrete, reinforcement, RC slabs, balconies, stairs, block partitions, windows and doors are by others (shown for coordination). Structural design (Turkish Building Earthquake Code), TS 825 and the fire regulation by the client's engineers.

QUOTATION - NOT FOR CONSTRUCTION

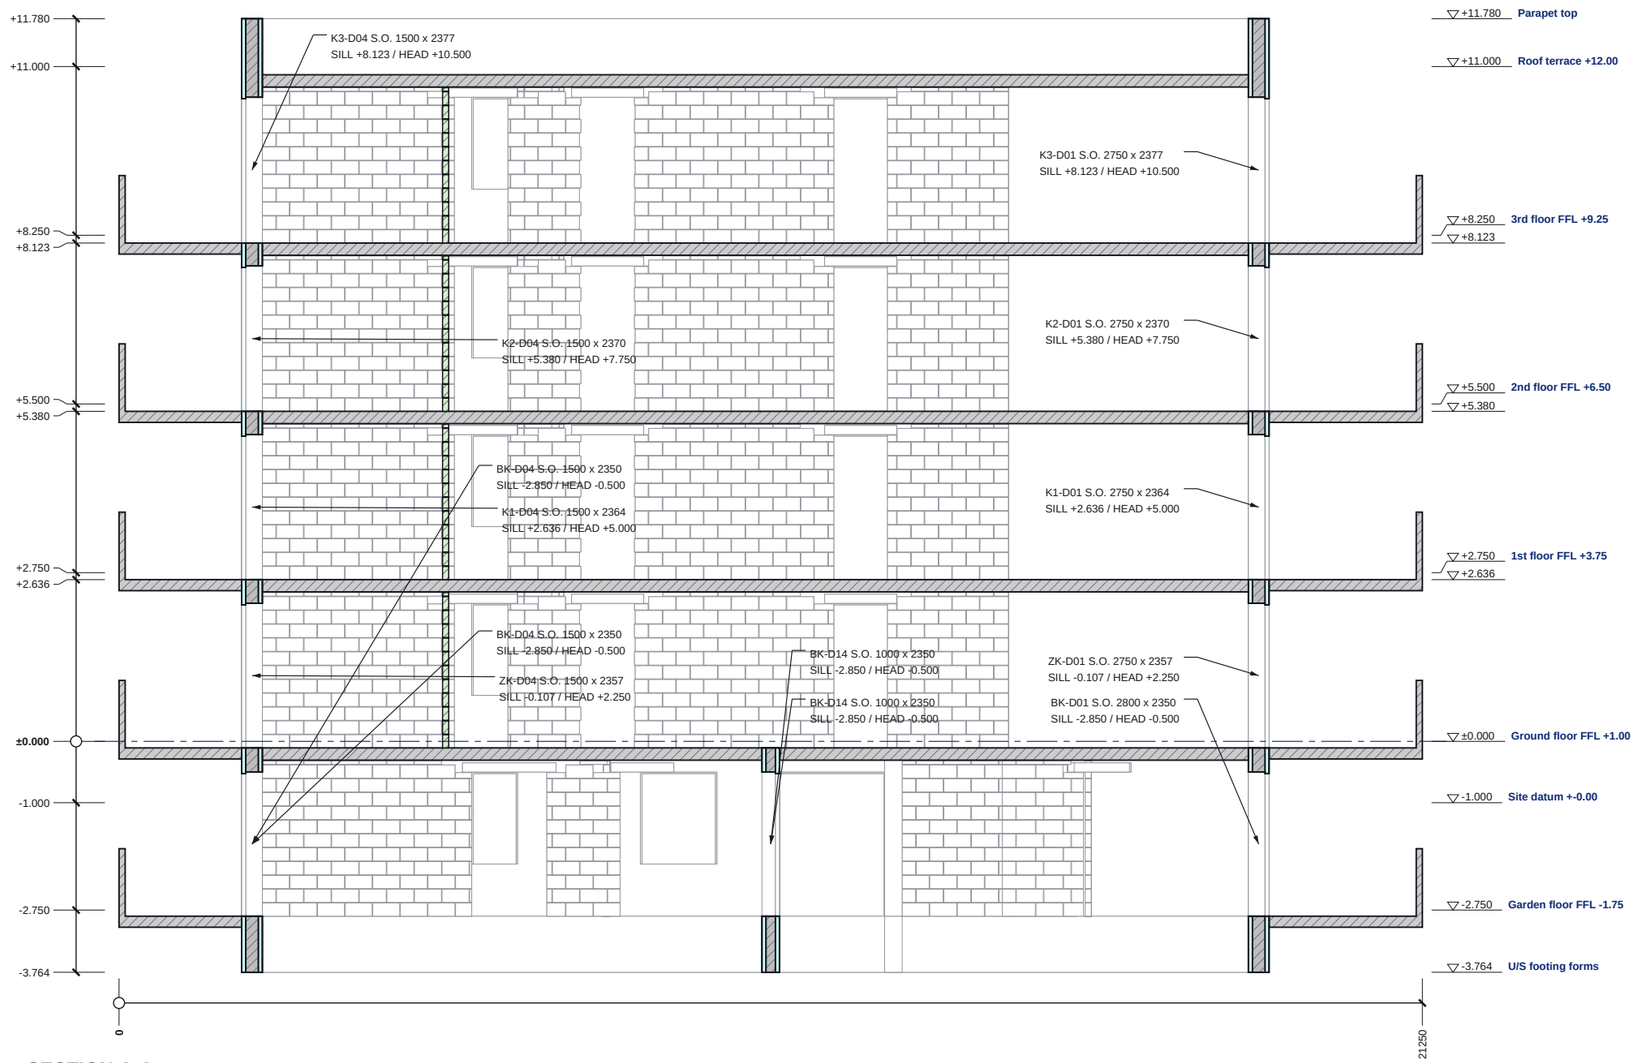

SECTION A-A

Scale 1:100 @ A3 | Looking west; levels above GF FFL

ICF EPS (cut)
ICF concrete core / RC (cut)
Steel (cut)
Masonry wall (cut)
Beyond the cut (line work)


0 1 2 3 4 5m

SECTION A-A SCHEDULES

LEVELS ON THIS SECTION

Level	FFL
U/S footing forms	-3.764
Garden floor FFL -1.75	-2.750
Site datum +-0.00	-1.000
Ground floor FFL +1.00	±0.000
top of ICF W04	+2.636
1st floor FFL +3.75	+2.750
top of ICF W04	+5.380
2nd floor FFL +6.50	+5.500
top of ICF W04	+8.123
3rd floor FFL +9.25	+8.250
Roof terrace +12.00	+11.000
Parapet top	+11.780

SECTION KEY

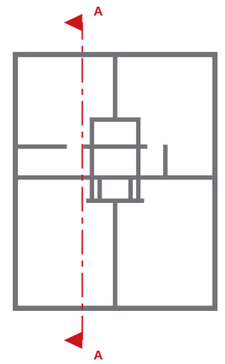

NOTES

1. Section A-A is a BuildEase ICF section (not an architect's section line). Cut elements hatched / filled; the model beyond the cut in line work.
2. Levels above GF FFL.
3. ICF: Nudura 8" Std, 66.7 EPS + 203.2 core + 66.7 EPS = 336.6; 6" Std, 66.7 EPS + 152.4 core + 66.7 EPS = 285.8, 203.2 core + 66.7 EPS = 336.6. No structural design issued (no building permit yet). ICF per the Arfa Yapi architectural set (sheets 02-14/14): every drawn 250 load-bearing wall in ICF - 8in Std (203 core = the 20 cm core asked for) external, 6in Std party / stair / lift walls; 20 cm in-situ RC slabs bearing into the cores. Reinforcement and the earthquake design by the client's engineer.
4. Steel marks, BOS / TOS: rev -. See ES26-085-GA-01 / EL-01 / EL-02 in the approval drawings pack.
5. Datum: +-0.00 = site datum (drawings); garden floor FFL -1.75, ground floor FFL +1.00, storeys 2.75 m.
6. ICF on the drawn outer face of the external walls (8in Std 337 v 250 drawn) - rooms lose 87 mm at the envelope.

REVISIONS

REV	DATE	DESCRIPTION
Q01	22.10.26	First issue - one block Rev C / 12 blocks Rev B

Nudura™ BuildEase

CLIENT	PROJECT
Arfa Yapi Sistemleri via Tremco CPG Turkey	Arfa Yapi apartment blocks, Bayrakli, Izmir - Block A1

DRAWING TITLE
SECTION A-A
ICF section with levels and build-ups

SCALE	SIZE	DATE
1:100	A3	22.10.26
DRAWN	CHECKED	APPROVED
TS		

STATUS	DRAWING No.	REV
QUOTATION	ES26-085-SE-01	Q01

Do not scale. All dimensions in millimetres, levels in metres from GF FFL. Check all dimensions on site.